
# POSTE TUBULAR 10.000 / 10Mb


**PLANO ESQUEMÁTICO · FABRICACIÓN Y EMBUTES**

## ELEVACIÓN / VISTA FRONTAL

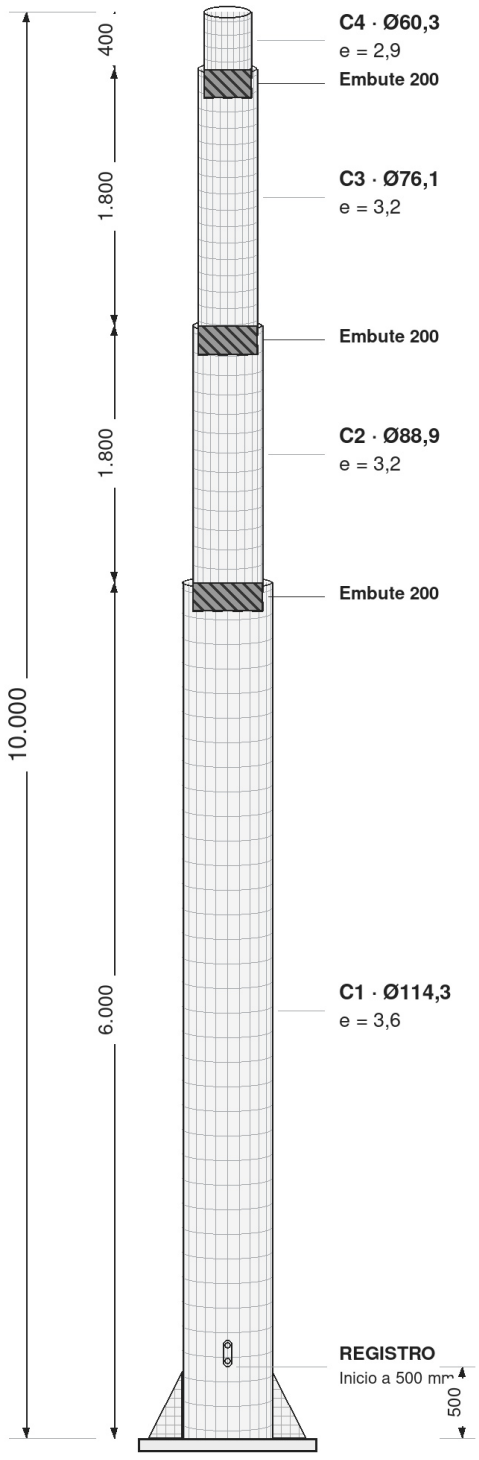


Diámetros ampliados para lectura. No escalar.


## DETALLE DEL EMBUTE

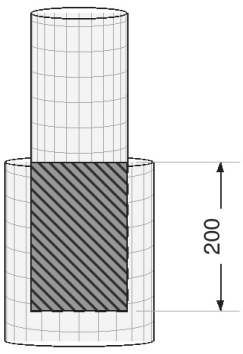


Achurado oscuro = embute dentro del cuerpo anterior.

**Los 200 mm están incluidos en el largo de corte.**


## ATIEZADOR / PERFIL

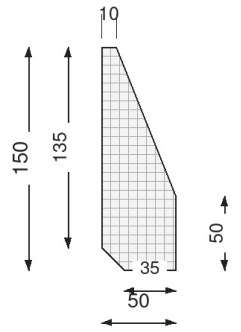


**4 unidades · espesor por definir.**

Perfil según detalle aportado.

## PLANTA DE PLACA BASE

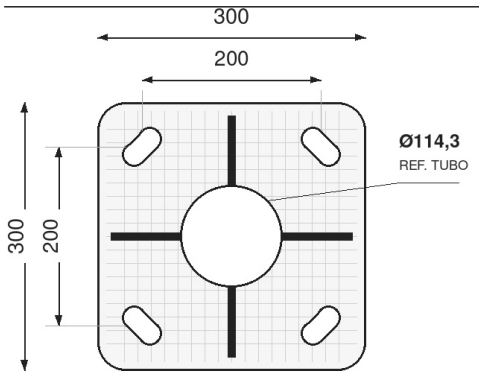



**PL300 · 300 × 300 × 12 mm**

**Orificio: AJUSTE A PRESIÓN, sin holgura.**

Tubo Ø114,3 · cota de corte e interferencia por definir.

## CANASTILLO / ANCLAJE

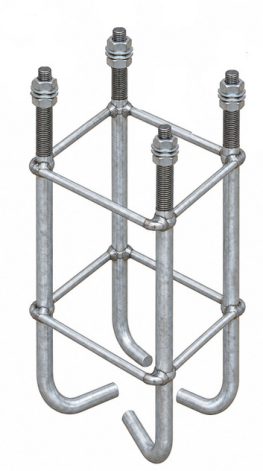

**Perno total:**
**500 mm**


**Hilo: 100 mm**

**Pata: 100 mm**
Puntas hacia el centro.

**4 pernos Ø3/4" × 500 mm · CAN3.4**

Radio de doblado por definir. Vista referencial.

## BASE Y TAPA DE REGISTRO / VISTA ISOMÉTRICA

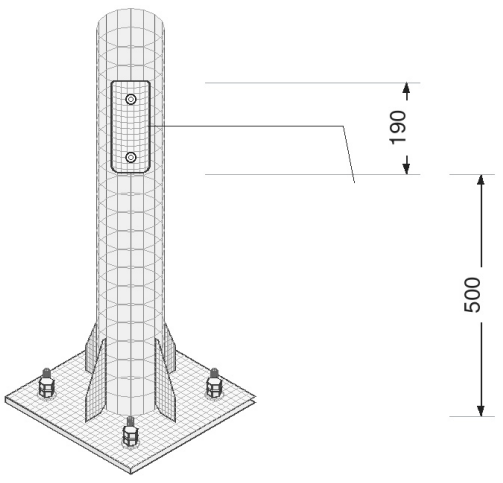


**TAPA DE REGISTRO**
**65 × 190 mm**
2 fijaciones

**Inicio: 500 mm**
sobre la placa.

Término: 690 mm

Placa, pernos, atiezadores y registro integrados. Cotas exteriores en mm. Vista sin escala.

## CONDICIONES ORBE

**EMBUTES**
Base sin embute. Desde C2: 200 mm.
El embute está incluido en el corte.

**COTAS**
Cuerpo visible + embute = corte total.
Cuerpos separados en vertical.

**REALCE**
Achurado oscuro en los 200 mm
que entran en el cuerpo anterior.


**PLACA Y PERNOS**
4 atiezadores en cruz, a 90°.
4 pernos centrados entre ellos, a 45°.

**PERFORACIONES / EJES**
Entrecéntro: 200 × 200 mm.
Ranuras diagonales entre atiezadores.

**ORIFICIO CENTRAL**
Ajuste a presión con la cañería base.
Interferencia y cota final por definir.

**REGISTRO**
65 × 190 mm. Inicio a 500 mm
desde la placa; termina a 690 mm.

## CUERPO VISIBLE + EMBUTE = TOTAL A CORTAR

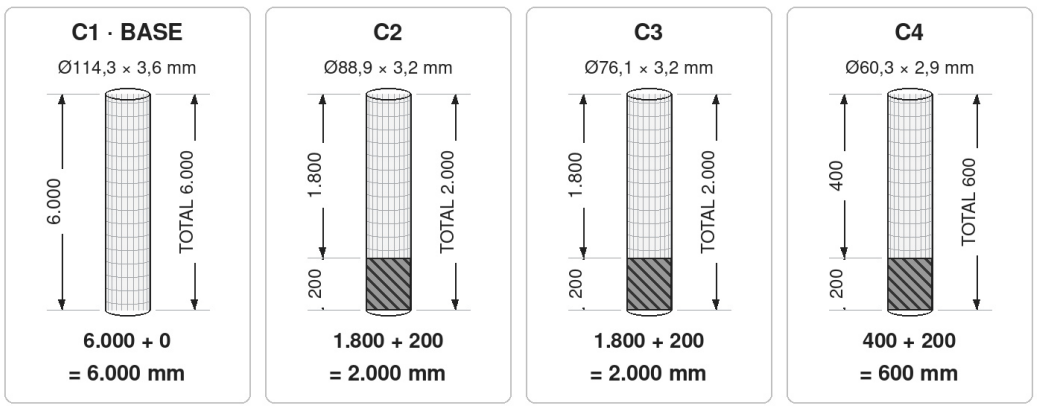


Embutidos: achurado oscuro. Cotas: visible + embute = total. Esquemas sin escala.

## ESPECIFICACIONES DE FABRICACIÓN

| Cuerpo | Norma | Ø (mm) | e (mm) | Visible (mm) | Corte (mm) | Embute (mm) |
|---|---|---|---|---|---|---|
| **C1 · BASE** | ISO R65 | 114,3 | 3,6 | 6.000 | **6.000** | 0 |
| **C2** | ISO R65 | 88,9 | 3,2 | 1.800 | **2.000** | 200 |
| **C3** | ISO R65 | 76,1 | 3,2 | 1.800 | **2.000** | 200 |
| **C4** | ISO R65 | 60,3 | 2,9 | 400 | **600** | 200 |

**ALTURA ARMADA: 10.000 mm**

**TOTAL CAÑERÍA A CORTAR: 10.600 mm**

Peso de cañerías: 85,8 kg · incluye embutes; excluye placa y atiezadores.

**Base sin embute. Cada cuerpo siguiente entra 200 mm en el anterior.**

Acabado: galvanizado ORBE. Barras de catálogo: 6.000 mm.

**PLANO PRELIMINAR · COTAS EN mm · TRAZADO SIN ESCALA**

Validación estructural normativa pendiente. Placa y anclaje: disposición referencial.

**ORBE**
**10Mb / REV. M**