
POSTE TUBULAR 12.000 / 12Ma


PLANO ESQUEMÁTICO · FABRICACIÓN Y EMBUTES

ELEVACIÓN / VISTA FRONTAL

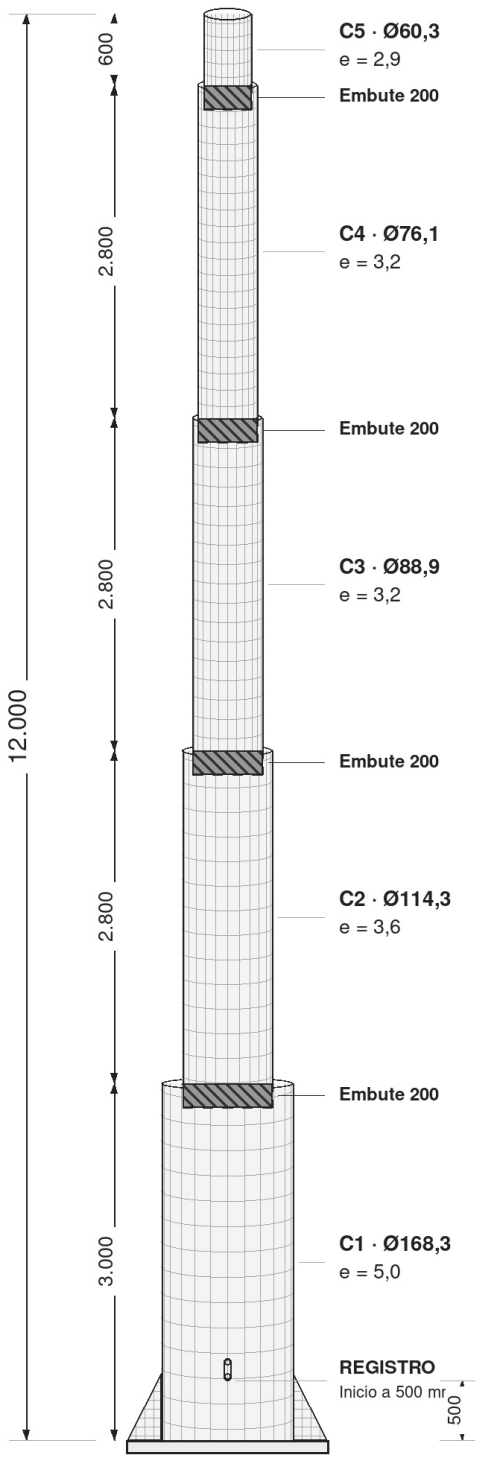

Diámetros ampliados para lectura. No escalar.


DETALLE DEL EMBUTE

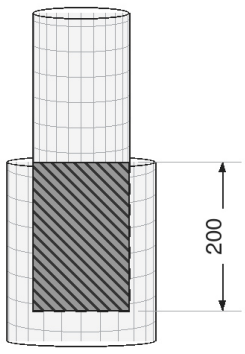

Achurado oscuro = embute dentro del cuerpo anterior.

Los 200 mm están incluidos en el largo de corte.


ATIEZADOR / PERFIL

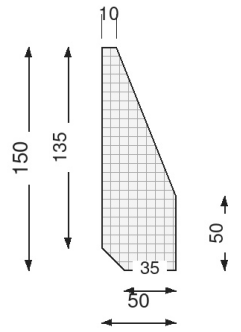

4 unidades · espesor por definir.

Perfil según detalle aportado.

PLANTA DE PLACA BASE

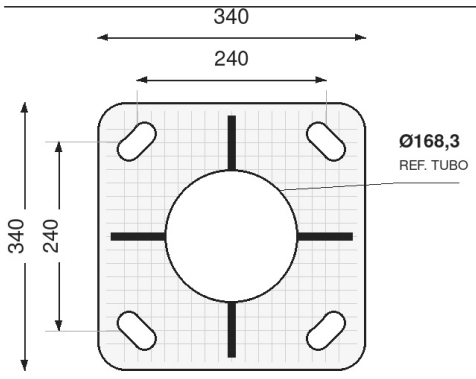


PL340 · 340 × 340 × 12 mm

Orificio: AJUSTE A PRESIÓN, sin holgura.

Tubo Ø168,3 · cota de corte e interferencia por definir.

CANASTILLO / ANCLAJE

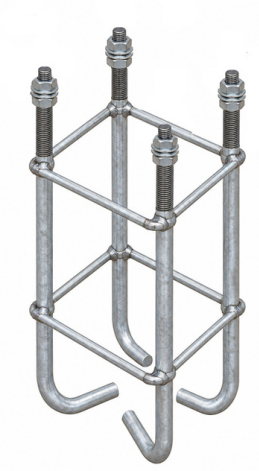

Perno total:
500 mm


Hilo: 100 mm

Pata: 100 mm
Puntas hacia el centro.

4 pernos Ø7/8" × 500 mm · CAN7.8

Radio de doblado por definir. Vista referencial.

BASE Y TAPA DE REGISTRO / VISTA ISOMÉTRICA

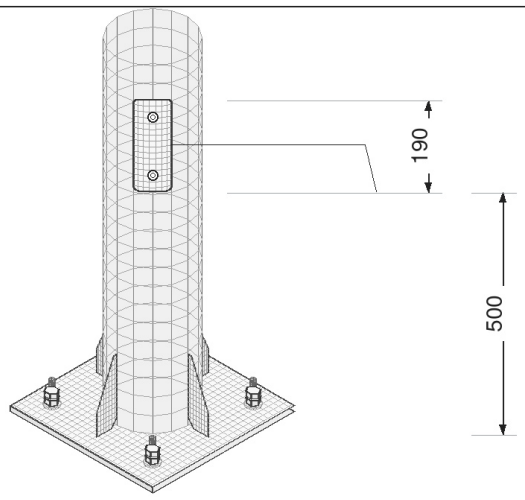

TAPA DE REGISTRO
65 × 190 mm
2 fijaciones

Inicio: 500 mm
sobre la placa.

Término: 690 mm

Placa, pernos, atiezadores y registro integrados. Cotas exteriores en mm. Vista sin escala.

CONDICIONES ORBE

EMBUTES
Base sin embute. Desde C2: 200 mm.
El embute está incluido en el corte.

COTAS
Cuerpo visible + embute = corte total.
Cuerpos separados en vertical.

REALCE
Achurado oscuro en los 200 mm
que entran en el cuerpo anterior.


PLACA Y PERNOS
4 atiezadores en cruz, a 90°.
4 pernos centrados entre ellos, a 45°.

PERFORACIONES / EJES
Entrecéntro: 240 × 240 mm.
Ranuras diagonales entre atiezadores.

ORIFICIO CENTRAL
Ajuste a presión con la cañería base.
Interferencia y cota final por definir.

REGISTRO
65 × 190 mm. Inicio a 500 mm
desde la placa; termina a 690 mm.

CUERPO VISIBLE + EMBUTE = TOTAL A CORTAR

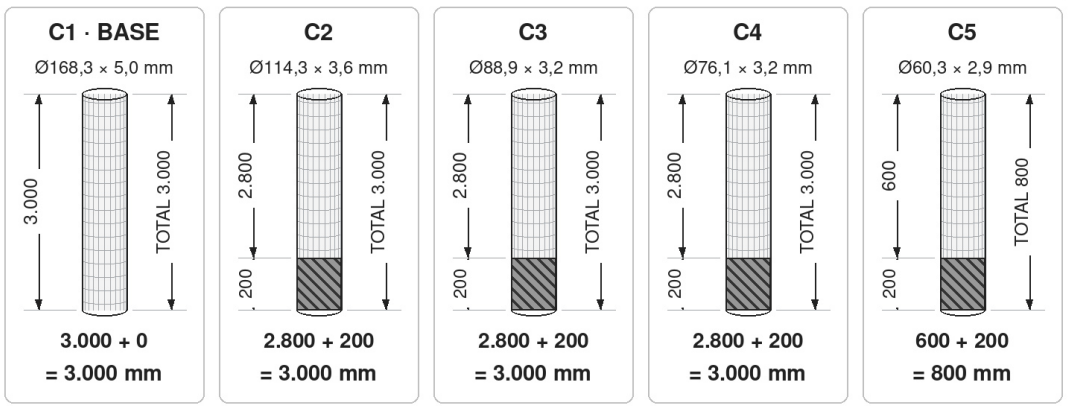

Embutidos: achurado oscuro. Cotas: visible + embute = total. Esquemas sin escala.

ESPECIFICACIONES DE FABRICACIÓN

Cuerpo	Norma	Ø (mm)	e (mm)	Visible (mm)	Corte (mm)	Embute (mm)
C1 · BASE	ASTM A53	168,3	5,0	3.000	**3.000**	0
C2	ISO R65	114,3	3,6	2.800	**3.000**	200
C3	ISO R65	88,9	3,2	2.800	**3.000**	200
C4	ISO R65	76,1	3,2	2.800	**3.000**	200
C5	ISO R65	60,3	2,9	600	**800**	200

ALTURA ARMADA: 12.000 mm

TOTAL CAÑERÍA A CORTAR: 12.800 mm

Peso de cañerías: 129,8 kg · incluye embutes; excluye placa y atiezadores.

Base sin embute. Cada cuerpo siguiente entra 200 mm en el anterior.

Acabado: galvanizado ORBE. Barras de catálogo: 6.000 mm.

PLANO PRELIMINAR · COTAS EN mm · TRAZADO SIN ESCALA

Validación estructural normativa pendiente. Placa y anclaje: disposición referencial.

ORBE
12Ma / REV. M