
POSTE TUBULAR 4.000 / 4Ma


PLANO ESQUEMÁTICO · FABRICACIÓN Y EMBUTES

ELEVACIÓN / VISTA FRONTAL

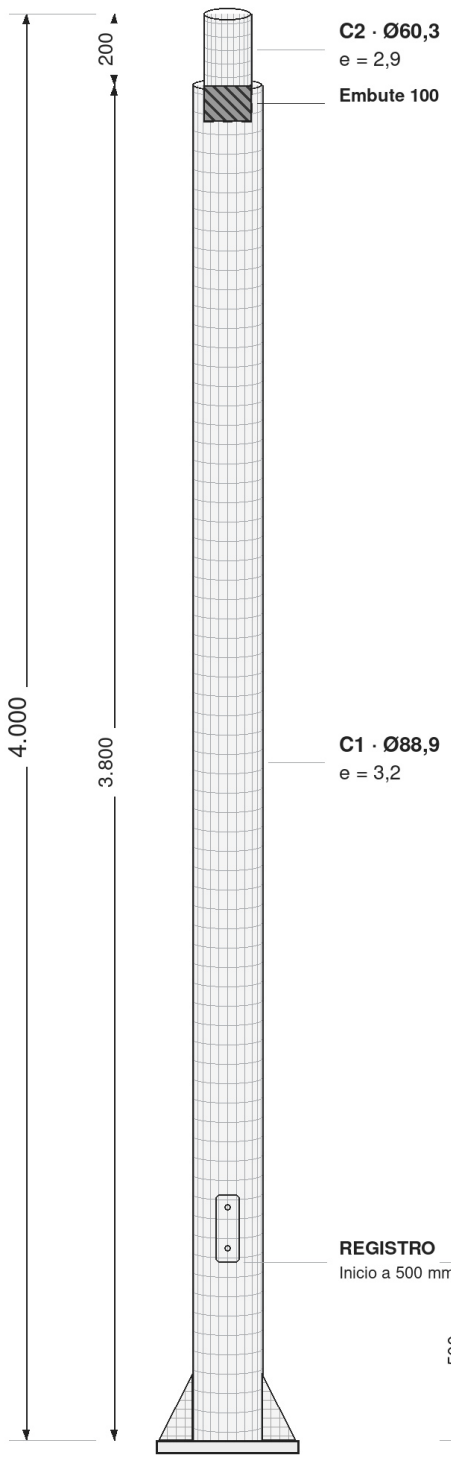

Diámetros ampliados para lectura. No escalar.


REDUCCIÓN SUPERIOR / EMBUTE

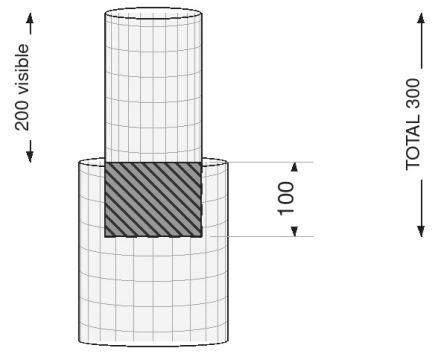

Achurado oscuro = embute dentro del cuerpo anterior.

100 mm embutidos + 200 mm visibles = 300 mm.


ATIEZADOR / PERFIL

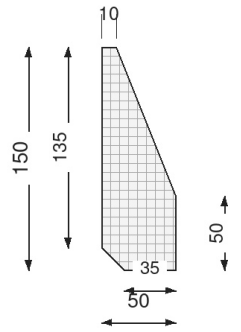

4 unidades · espesor por definir.

Perfil según detalle aportado.

PLANTA DE PLACA BASE

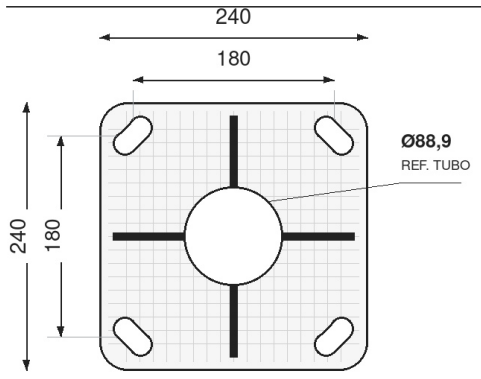


PL240 · 240 × 240 × 10 mm

Orificio: AJUSTE A PRESIÓN, sin holgura.

Tubo Ø88,9 · cota de corte e interferencia por definir.

CANASTILLO / ANCLAJE

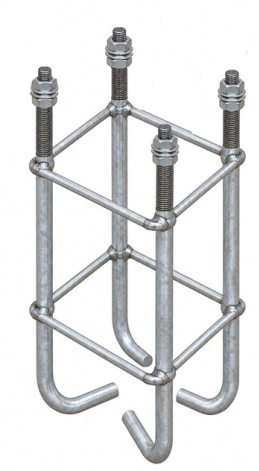

Perno total:
500 mm


Hilo: 100 mm

Pata: 100 mm
Puntas hacia el centro.

4 pernos Ø5/8" × 500 mm · CAN5.8

Radio de doblado por definir. Vista referencial.

BASE Y TAPA DE REGISTRO / VISTA ISOMÉTRICA

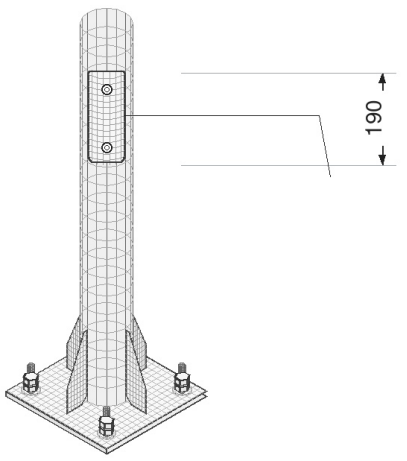

TAPA DE REGISTRO
65 × 190 mm
2 fijaciones

Inicio: 500 mm
sobre la placa.

Término: 690 mm

Placa, pernos, atiezadores y registro integrados. Cotas exteriores en mm. Vista sin escala.

CONDICIONES ORBE

REDUCCIÓN DE 3 A 6 m
100 mm embutidos + 200 mm visibles.
Corte de reducción: 300 mm.

COTAS EXTERIORES
Todas las cotas fuera del dibujo.
Cuerpo visible + embute = total.

PERNO / CANASTILLO
Total de barra: 500 mm. Hilo: 100 mm.
Pata de 100 mm apuntando al centro.


PLACA Y PERNOS
4 atiezadores en cruz, a 90°.
4 pernos centrados entre ellos, a 45°.

PERFORACIONES / EJES
Entrecéntro: 180 × 180 mm.
Ranuras diagonales entre atiezadores.

ORIFICIO CENTRAL
Ajuste a presión con la cañería base.
Interferencia y cota final por definir.

REGISTRO
65 × 190 mm. Inicio a 500 mm
desde la placa; termina a 690 mm.

CUERPO VISIBLE + EMBUTE = TOTAL A CORTAR

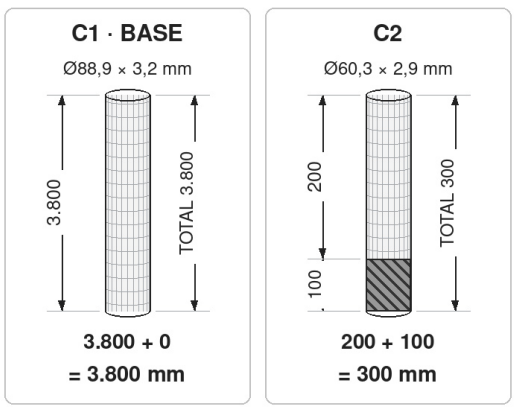

Embutidos: achurado oscuro. Cotas: visible + embute = total. Esquemas sin escala.

ESPECIFICACIONES DE FABRICACIÓN

Cuerpo	Norma	Ø (mm)	e (mm)	Visible (mm)	Corte (mm)	Embute (mm)
C1 · BASE	ISO R65	88,9	3,2	3.800	**3.800**	0
C2	ISO R65	60,3	2,9	200	**300**	100

ALTURA ARMADA: 4.000 mm

TOTAL CAÑERÍA A CORTAR: 4.100 mm

Peso de cañerías: 26,8 kg · incluye embutes; excluye placa y atiezadores.

Cuerpo base sin embute. Reducción superior: 100 mm dentro + 200 mm fuera.

Acabado: galvanizado ORBE. Barras de catálogo: 6.000 mm.

PLANO PRELIMINAR · COTAS EN mm · TRAZADO SIN ESCALA

Validación estructural normativa pendiente. Placa y anclaje: disposición referencial.

ORBE
4Ma / REV. M